




s:\kf projects\s-ranch\2 cad and drawings\8-plinksters\10\xx_s-ranch_details_bar window Plotted: 10/22/2025 4:26 PM

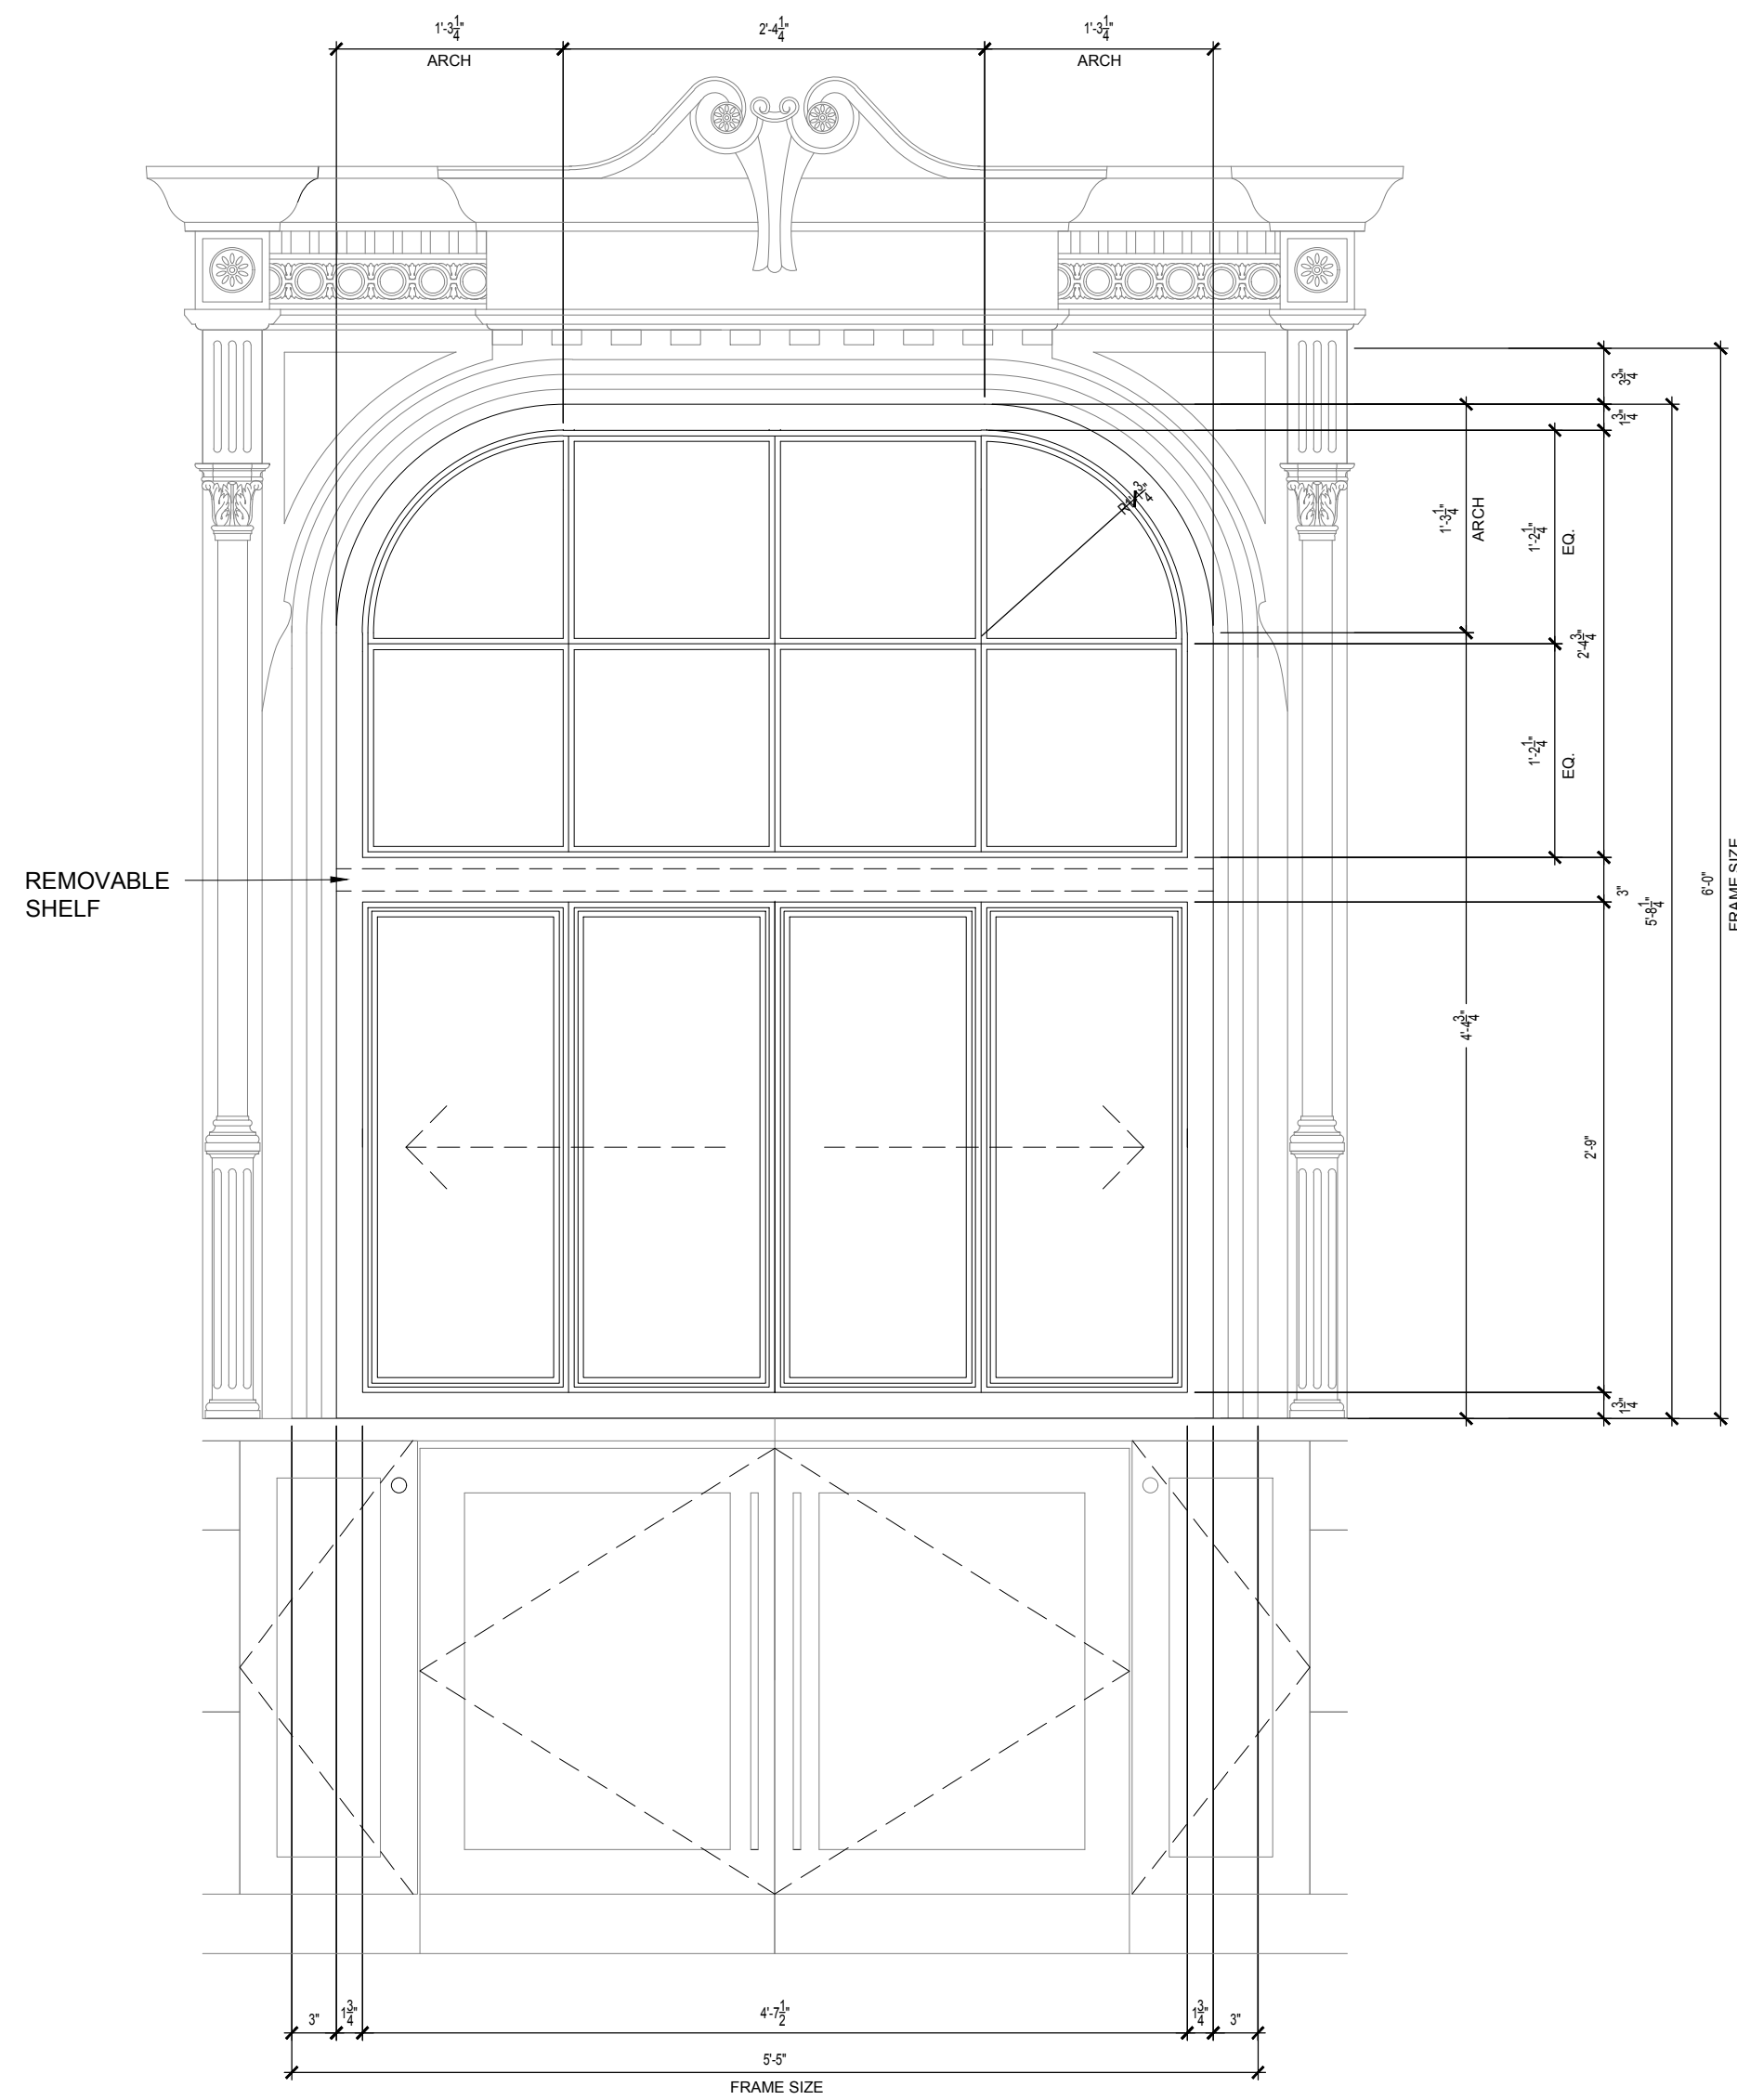

X BAR WINDOW - ENLARGED ELEVATION
SCALE: 1" = 1'-0"

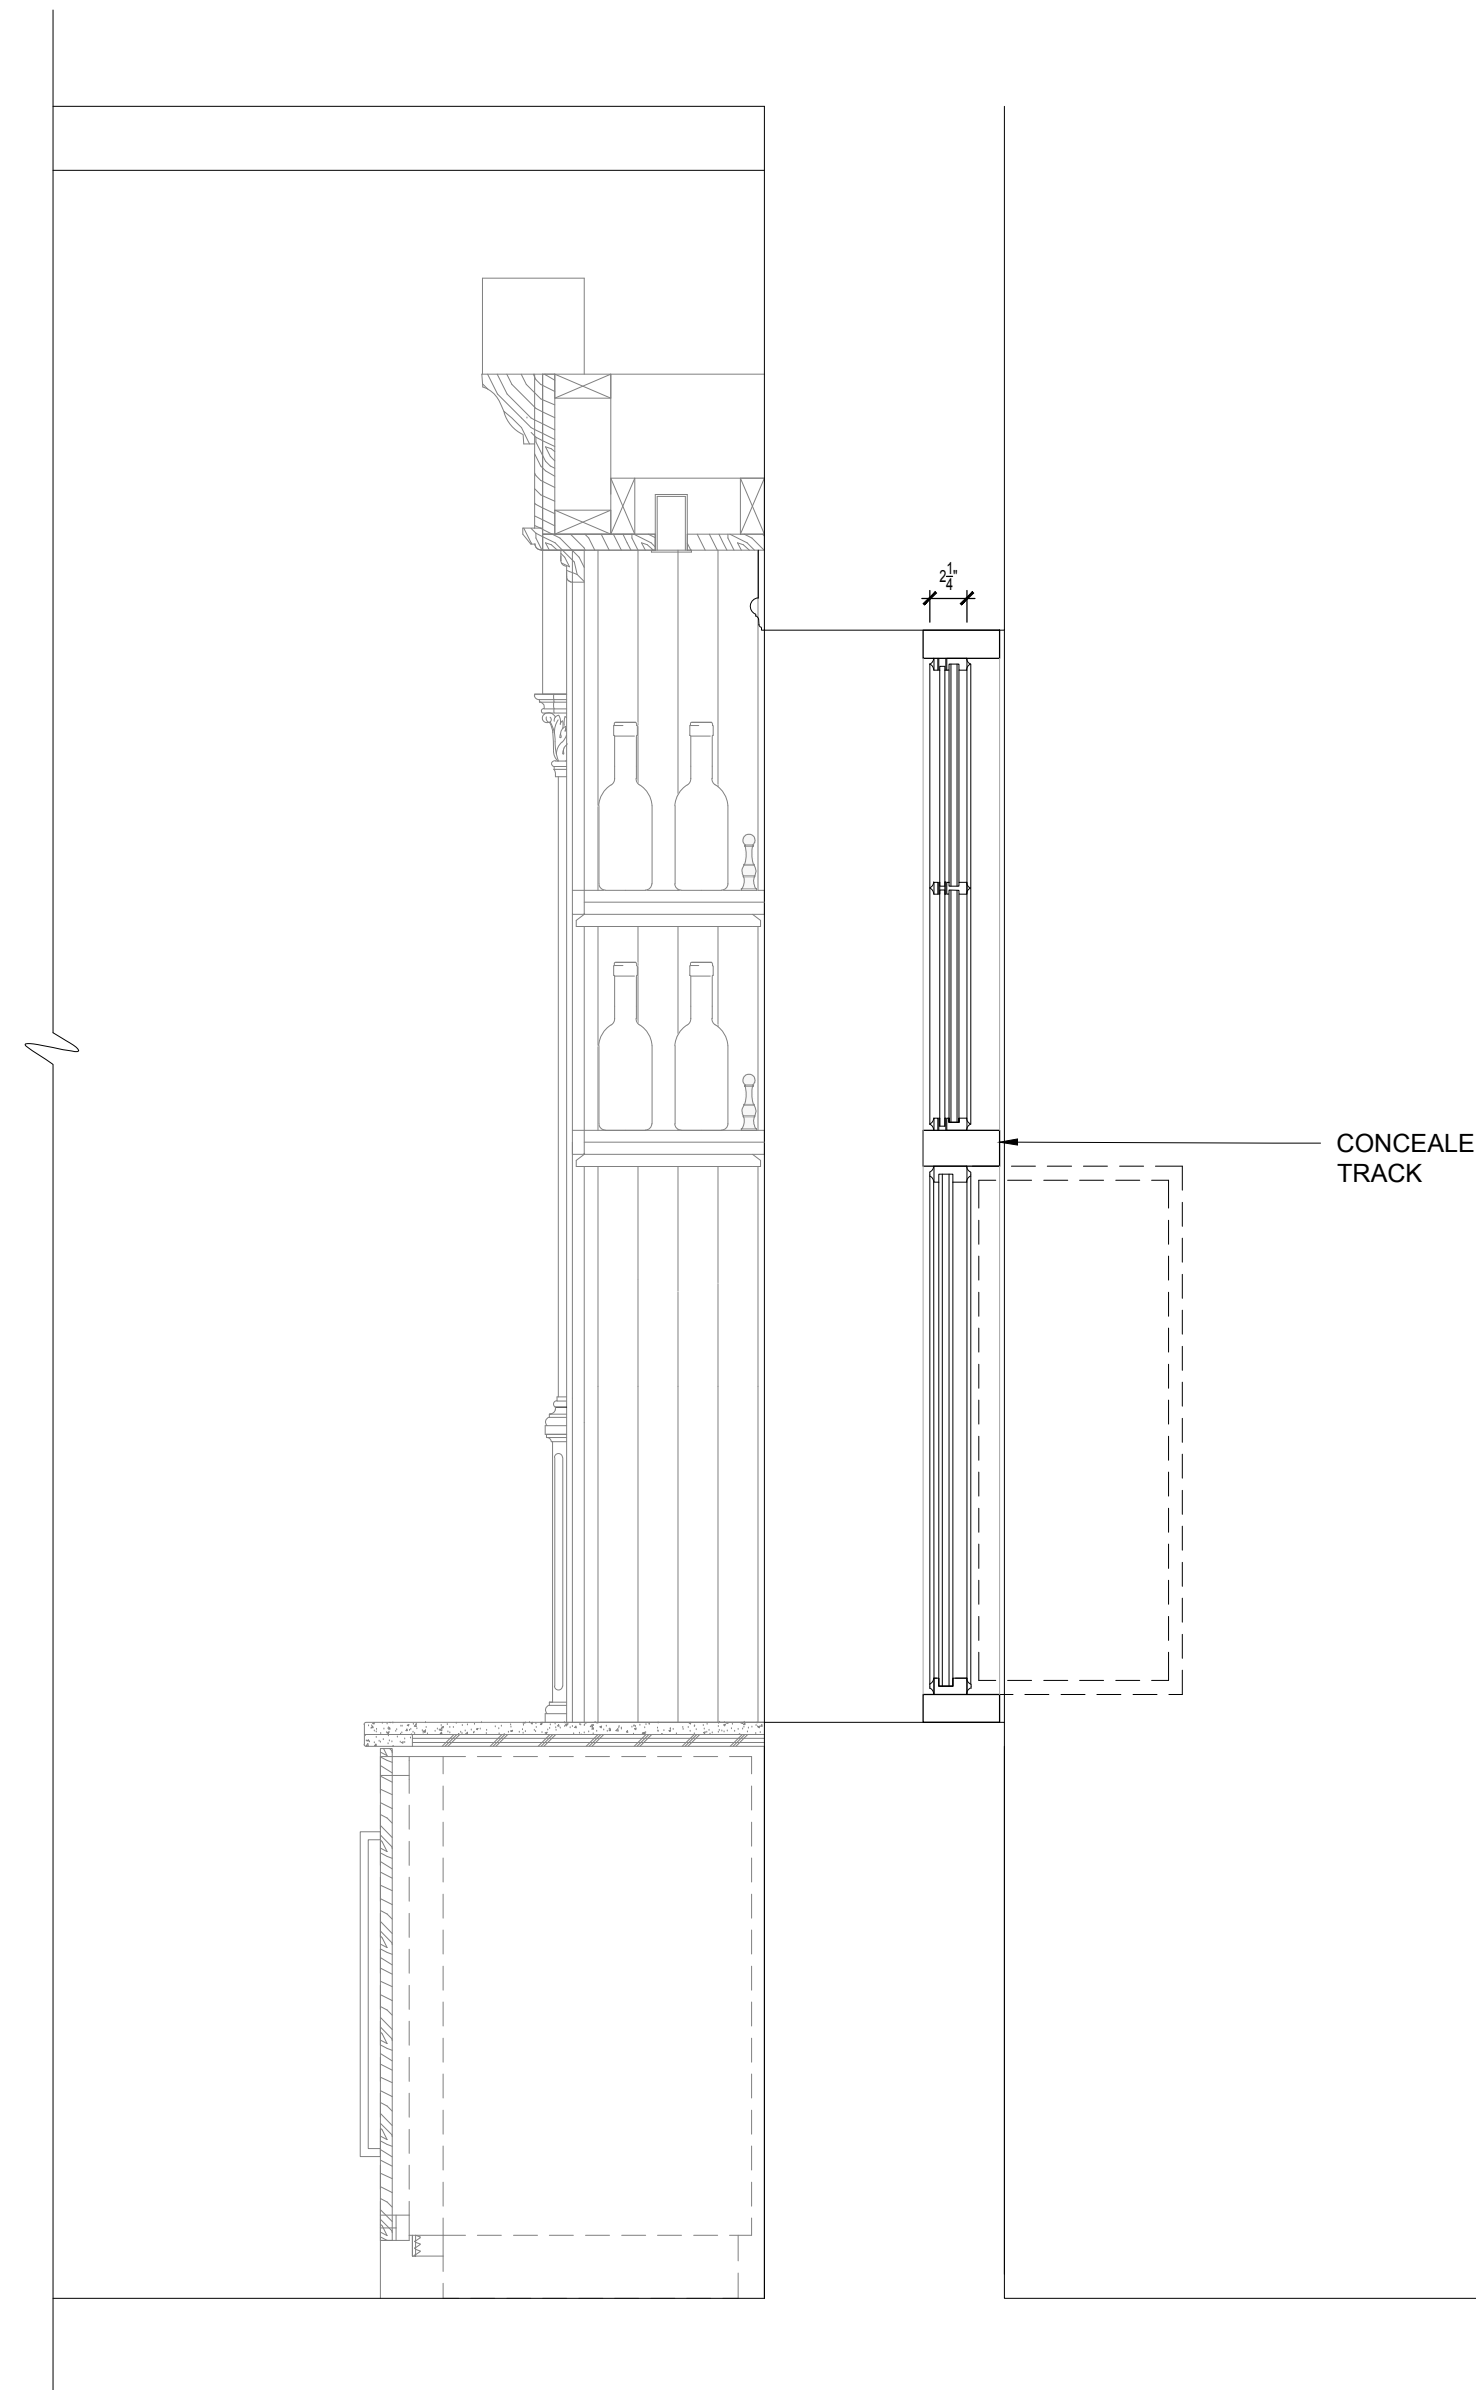

X BAR WINDOW - SECTION
SCALE: 1" = 1'-0"

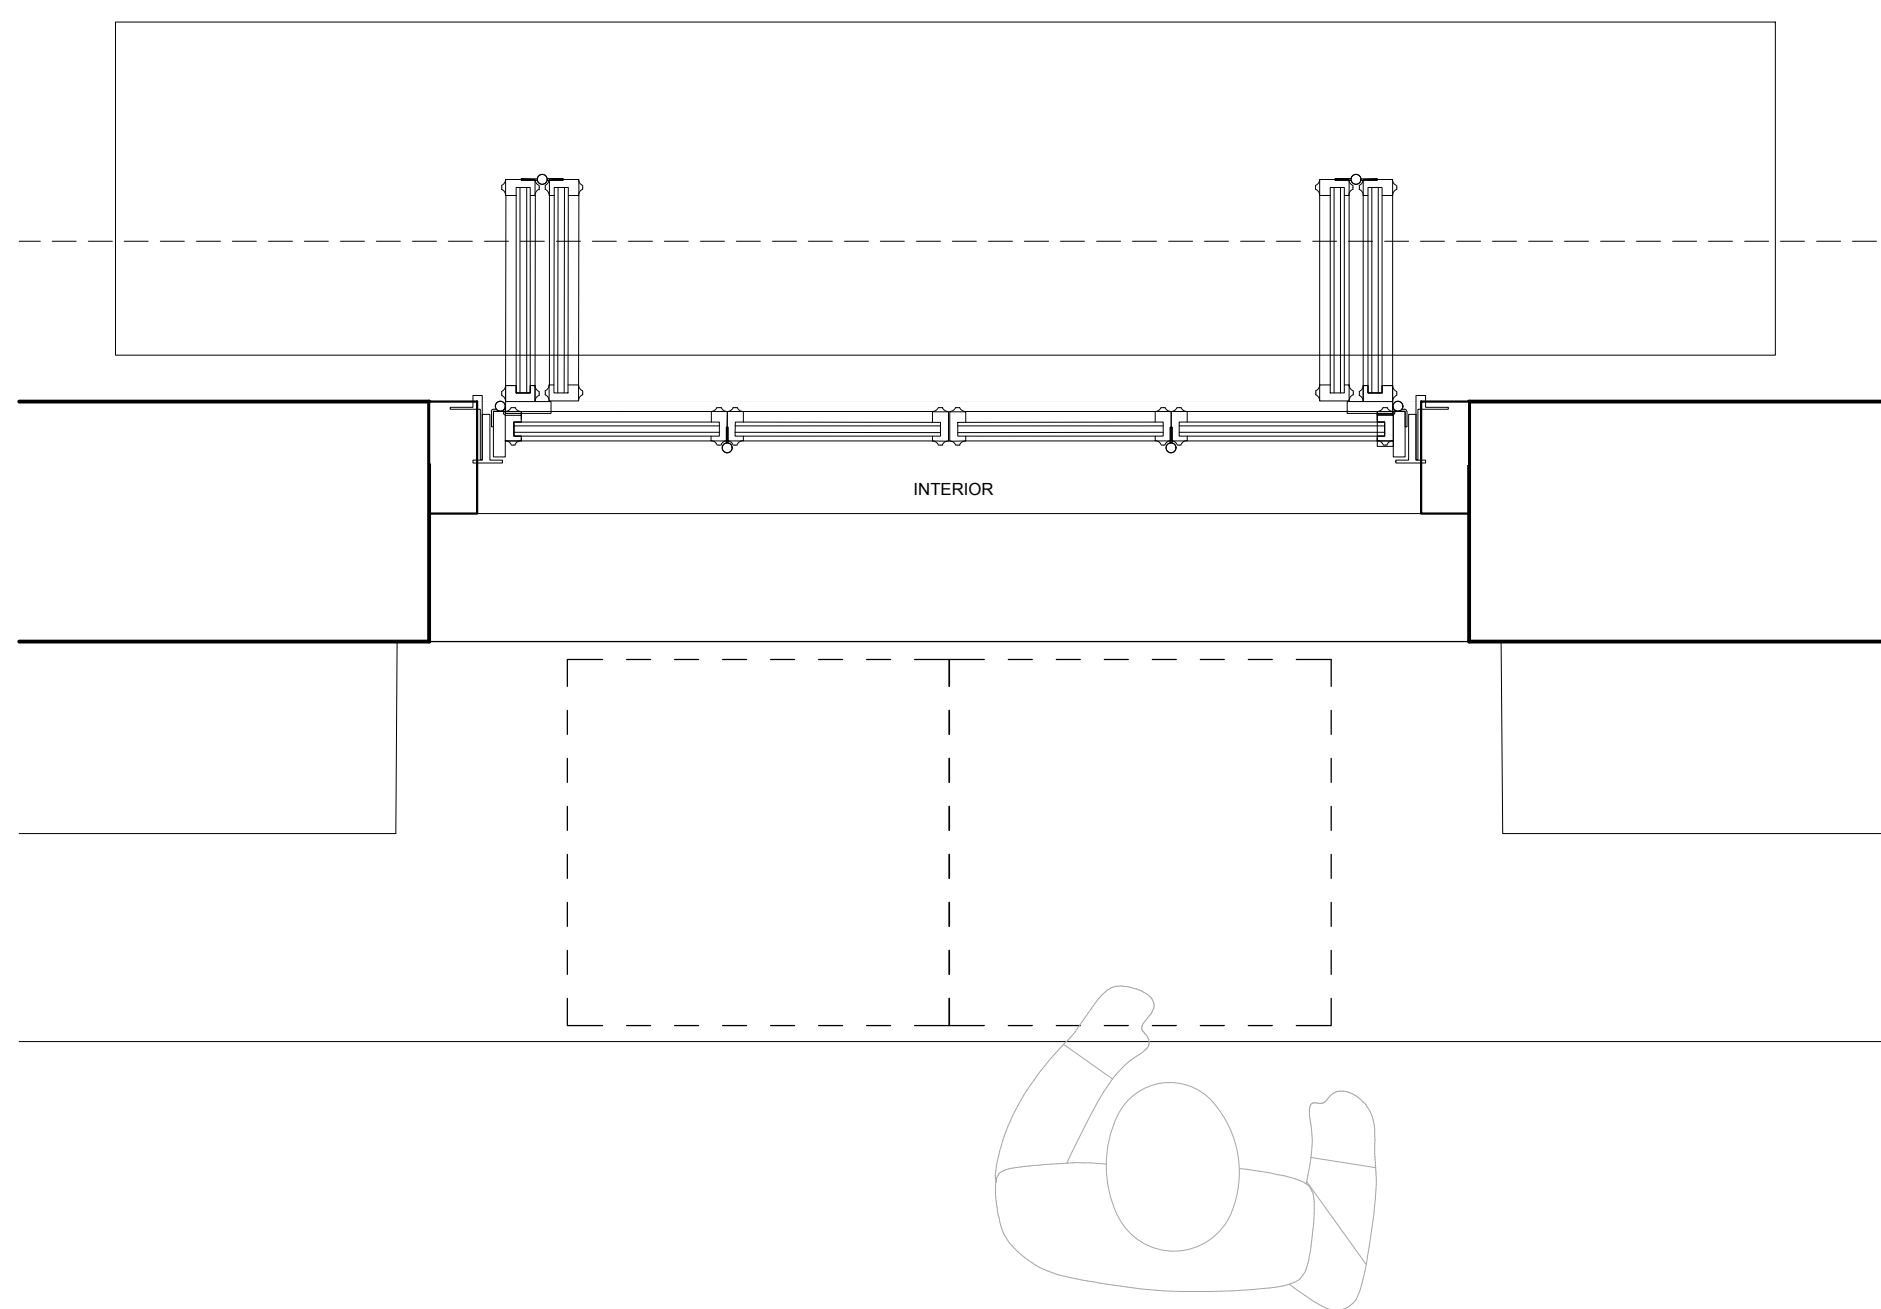

X BAR WINDOW - PLAN
SCALE: 1" = 1'-0"



KEN FULK

EST. 1997

310 SEVENTH ST. SAN FRANCISCO 94103
T 415.285.1164 F 415.285.1174 KENFULK.COM

S-RANCH
BOX ELDER RANCH
41 VT TRAIL
HILGER, MT 59451

COORDINATION DRAWINGS
NOT FOR CONSTRUCTION

Date Issued for:

BAR WINDOW DETAILS

Project No. S-RANCH
Project Path S:\KF\PROJECTS\S-RANCH
Date 09.26.2025
Scale AS NOTED
Drawn By JH/ST/JW
Checked By JH
Package No. Sheet No.

DD

IA9.XX

Ken Fulk, Inc. c 2019