Xref ..\2-Plans\1X_BASE_S-RANCH.dwg

DIM-STYLES:

DIM-01 (1'-0" = 1'-0")
DIM-02 (6" = 1'-0")
DIM-04 (3" = 1'-0")
DIM-08 (1 1-2" = 1'-0")
DIM-12 (1" = 1'-0")
DIM-16 (3/4" = 1'-0")
DIM-24 (1/2" = 1'-0")
DIM-32 (3/8" = 1'-0")
TEXT 4'-7½" DIM-48 (1/4" = 1'-0")
TEXT 4'-11½" DIM-64 (3/16" = 1'-0")
TEXT 5'-3½" DIM-96 (1/8" = 1'-0")
TEXT 5'-9" DIM-128 (3/32" = 1'-0")

PLOTSTYLE: 2021 KFI Pens.ctb

🟥 I-01
🟥 I-01H HIDDEN LINE
🟥 I-01 BASE (TURN OFF IN RCP)
🟨 I-02
🟩 I-03
🟦 I-04
🟦 I-05
🟪 I-06
I-06X
⬛ I-07
▨ I-08
▨ I-08H
▨ I-09
🟥 I-10 PRINTS RED
🟥 I-11

🟨 I-Anno
▨ I-Anno-NIC
🟩 I-Dims
🟨 I-Door
🟥 I-Elev
🟨 I-Equip

🟥 I-Patt - Floor Pattern
🟩 I-Fixt
🟥 I-Fixt-Hidden
🟩 I-Furn
🟥 I-Furn-Hidden
🟦 I-Mill
▨ I-Mill-Hidden
▨ I-Patt
🟨 I-Strs
🟪 I-Wall
🟨 I-Mill-Low
I-Wall-Fill
▨ X-Area
🟥 Xref

SYMBOLS

Annotation blocks (scale up by DIM-scale value)

KFI STANDARD Text Styles: (DDSTYLE)

_KFI-DIMs Dimension text

_KFI-TEXT Notes, text

_KFI-TITLES Dwg. Detail Titles

NOTE: ALL ANNOTATIVE TEXT SHOULD BE 3/32" TALL WHEN IT APPEARS ON A SHEET.

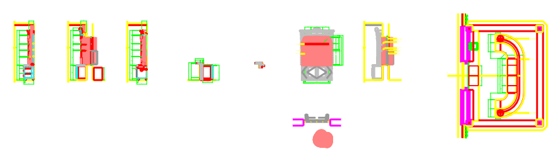

Xref ..\2-Plans\1X_FURN_S-RANCH.dwg

KEN FULK

EST. 1997

310 SEVENTH ST. SAN FRANCISCO 94103
T 415.285.1164 F 415.285.1174 KENFULK.COM

Drawing Title: PARTIAL IMAGE OF XXXXXXXXXXX			Dwg. No. 00 Page # of #
Project Name XXXXX		Project No. ####.##	
Scale #"=1'-0"	Drawn By XXX	Revision Date dd MON yy	Issue Date dd MON yy

Ken Fulk, Inc. c 2023 c:\users\jonathan house\onedrive - kenfulk\desktop\s ranch_window cad export Plotted: 5/4/2026 5:07 PM

KEN FULK
EST. 1997
310 SEVENTH ST. SAN FRANCISCO 94103
T 415.285.1164 F 415.285.1174 KENFULK.COM

Drawing Title: PARTIAL IMAGE OF
XXXXXXXXXXX
Project Name
XXXXX
Project No.
####.##
Scale
#"=1'-0"
Drawn By
XXX
Revision Date
dd MON yy
Issue Date
dd MON yy
Dwg. No.
00
Page # of #

Ken Fulk, Inc. c 2023 \users\jonathan house\onedrive - kenfulk\desktop\s ranch_window cad export Plotted: 5/4/2026 5:07 PM

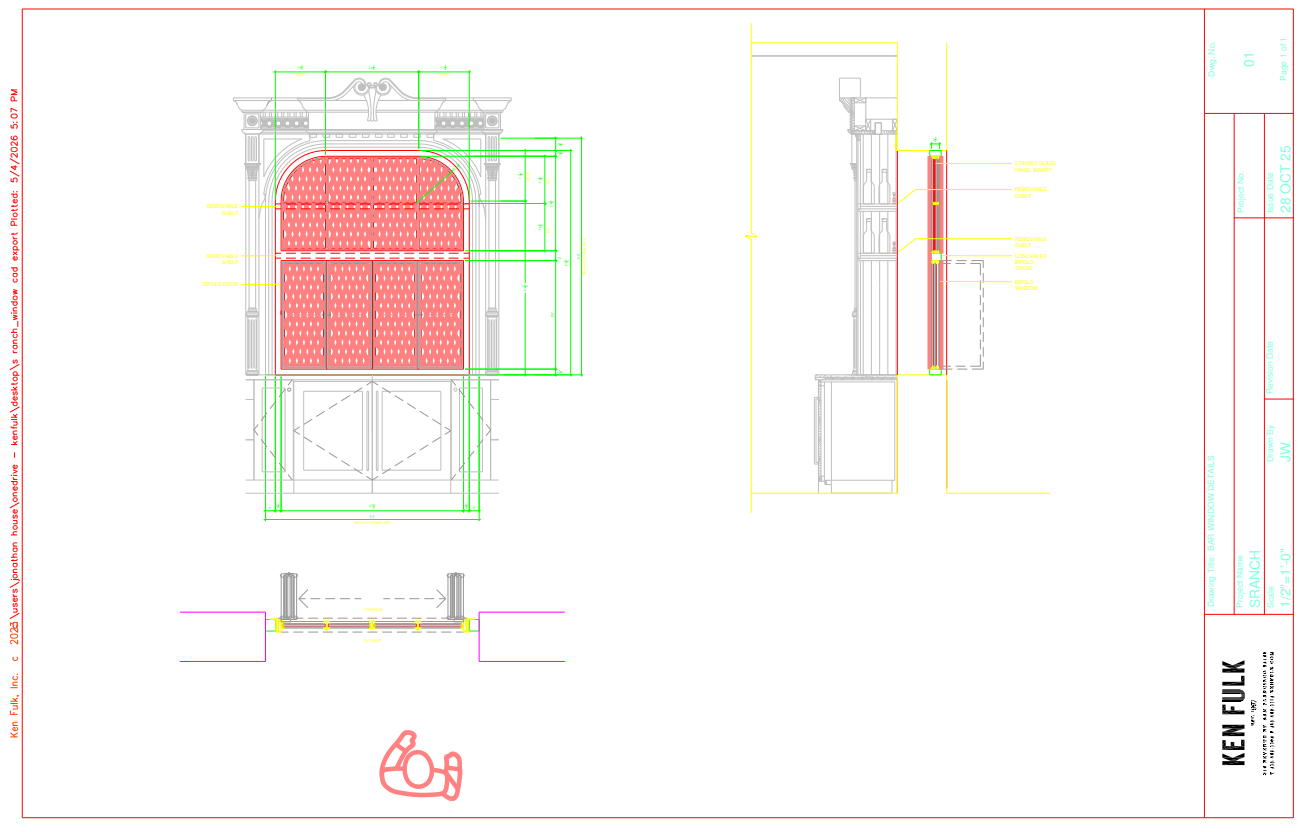
REMOVABLE SHELF
REMOVABLE SHELF
BIFOLD DOOR
STAINED GLASS PANEL INSERT
REMOVABLE SHELF
REMOVABLE SHELF
CONCEALED BIFOLD TRACK
BIFOLD WINDOW
EXTERIOR
INTERIOR

KEN FULK
EST. 1997
310 SEVENTH ST SAN FRANCISCO 94103
T 415.285.1164 F 415.285.1174 KENFULK.COM

Drawing Title: BAR WINDOW DETAILS

Project Name
SRANCH

Project No.

Scale
1/2"=1'-0"

Drawn By
JW

Revision Date

Issue Date
28 OCT 25

Dwg. No.
01

Page 1 of 1

KEN FULK

EST. 1997

310 SEVENTH ST. SAN FRANCISCO 94103
T 415.285.1164 F 415.285.1174 KENFULK.COM

PARTIAL IMAGE OF
XXXXXXXXXXX

Project Name XXXXX		Project No. ####.##	Dwg. No. 00
Scale #"=1'-0" XXX	Revision Date dd MON yy	Issue Date dd MON yy	Page # of #

Ken Fulk, Inc. c 2023

c:\users\jonathan house\onedrive - kenfulk\desktop\s ranch_window cad export Plotted: 5/4/2026 5:07 PM

KEN FULK
EST. 1997
310 SEVENTH ST. SAN FRANCISCO 94103
T 415.285.1164 F 415.285.1174 KENFULK.COM

Drawing Title: PARTIAL IMAGE OF XXXXXXXXXX		
Project Name XXXXX		Project No. ####.##
Scale #"=1'-0" or #:#	Drawn By XXX	Revision Date dd MON yy
		Issue Date dd MON yy

Dwg. No.
00
Page # of #

KEN FULK
EST. 1997
310 SEVENTH ST. SAN FRANCISCO 94103
T 415.285.1164 F 415.285.1174 KENFULK.COM

Drawing Title: PARTIAL IMAGE OF
XXXXXXXXXX

Project Name
XXXXX

Project No.
####.##

Scale
#"=1'-0" or #:#

Drawn By
XXX

Revision Date
dd MON yy

Issue Date
dd MON yy

Dwg. No.
00

Page # of #